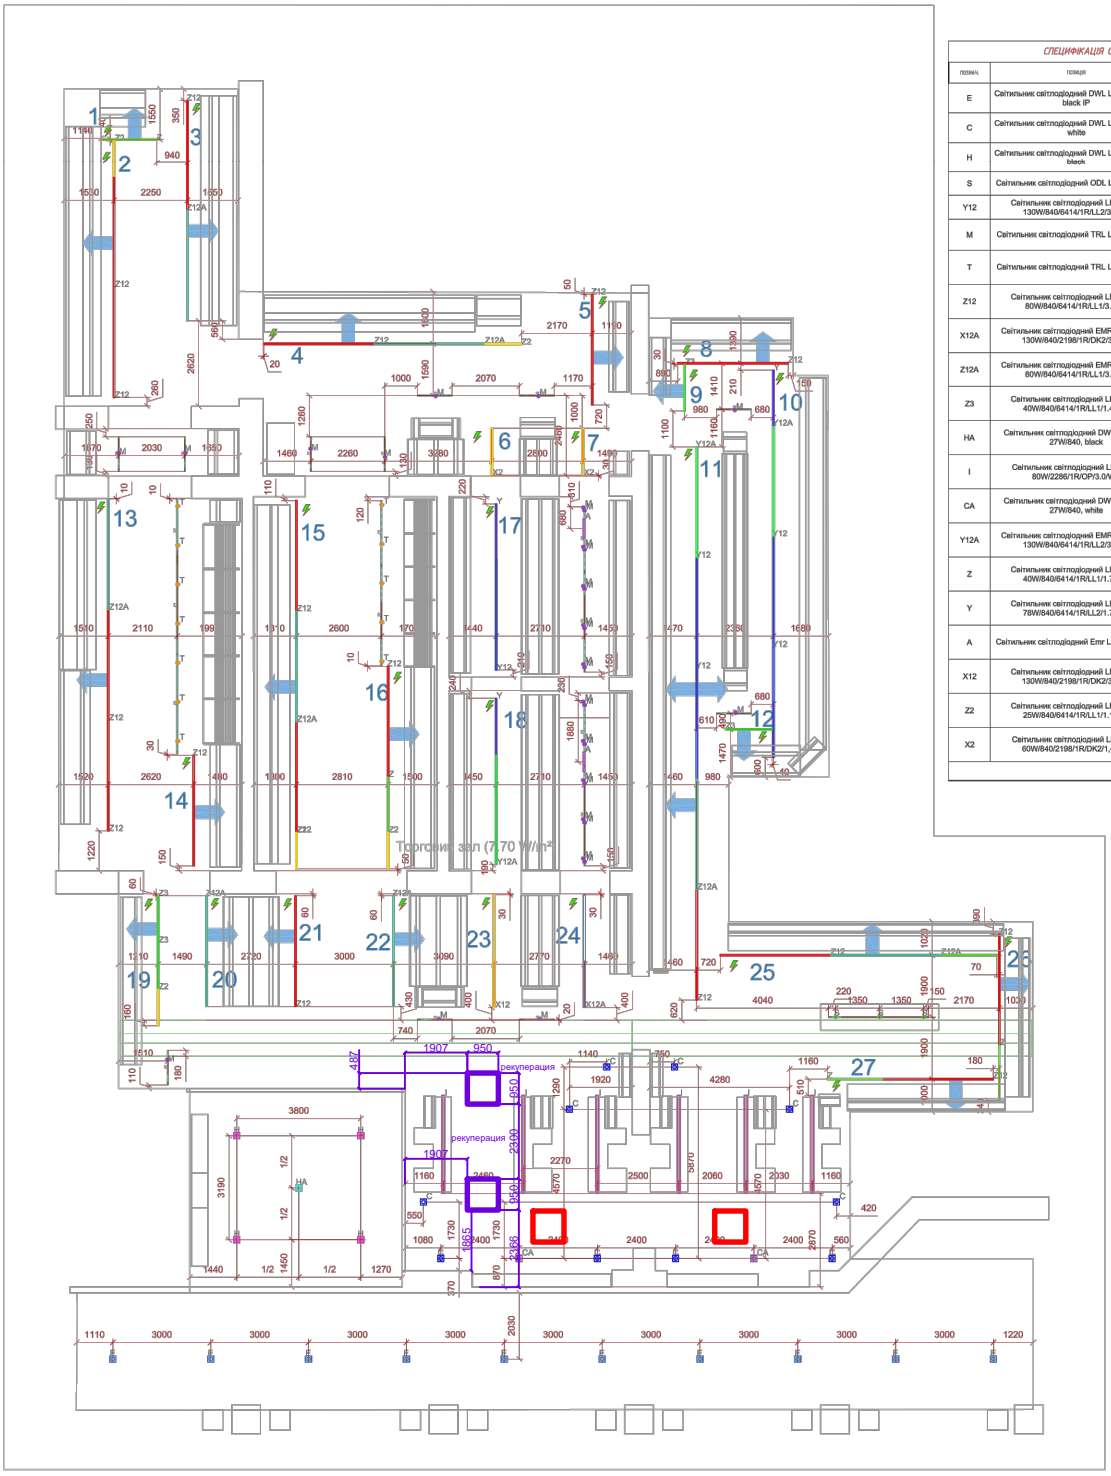

СПЕЦИФІКАЦІЯ ОСВІТЛЮВАЛЬНОГО ОБЛАДНАННЯ

ПОЗНАЧ.	ПОЗИЦІЯ	ВИД МОНТАЖУ	ПОТУЖНІСТЬ	К-СТЬ, ШТ	ЗАГАЛЬНА ПОТУЖНІСТЬ
E	Світильник світлодіодний DWL LED 22W/840, black IP	Вбудований	22	10	220
C	Світильник світлодіодний DWL LED 27W/840, white	Вбудований	27	10	270
H	Світильник світлодіодний DWL LED 27W/840, black	Вбудований	27	4	108
S	Світильник світлодіодний ODL LED 22W/840	Трековий	22	3	66
Y12	Світильник світлодіодний LINE LED 130W/840/6414/1R/LL2/3.4/BL	Підвісний	130	5	650
M	Світильник світлодіодний TRL LED 27W 840	Трековий	27	31	837
T	Світильник світлодіодний TRL LED 27W 830	Трековий	27	12	324
Z12	Світильник світлодіодний LINE LED 80W/840/6414/1R/LL1/3.4/BL	Підвісний	80	17	1360
X12A	Світильник світлодіодний EMR LINE LED 130W/840/2198/1R/DK2/3.4/BL	Підвісний	130	1	130
Z12A	Світильник світлодіодний EMR LINE LED 80W/840/6414/1R/LL1/3.4/BL	Підвісний	80	8	640
Z3	Світильник світлодіодний LINE LED 40W/840/6414/1R/LL1/1.43/BL	Підвісний	45	4	180
HA	Світильник світлодіодний DWL Emr LED 27W/840, black	Вбудований	27	1	27
I	Світильник світлодіодний LINE LED 80W/2286/1R/OP/3.0/WH	Підвісний	80	6	480
CA	Світильник світлодіодний DWL Emr LED 27W/840, white	Вбудований	27	2	54
Y12A	Світильник світлодіодний EMR LINE LED 130W/840/6414/1R/LL2/3.4/BL	Підвісний	130	3	390
Z	Світильник світлодіодний LINE LED 40W/840/6414/1R/LL1/1.72/BL	Підвісний	40	5	200
Y	Світильник світлодіодний LINE LED 78W/840/6414/1R/LL2/1.72/BL	Підвісний	78	3	234
A	Світильник світлодіодний Emr LINE black SH	Трековий	3	2	6
X12	Світильник світлодіодний LINE LED 130W/840/2198/1R/DK2/3.4/BL	Підвісний	130	1	130
Z2	Світильник світлодіодний LINE LED 25W/840/6414/1R/LL1/1.12/BL	Підвісний	25	5	125
X2	Світильник світлодіодний LINE LED 60W/840/2198/1R/DK2/1.43/BL	Підвісний	60	2	120
					6.551000

ПОЗНАЧ.	ПЛОЩА, м²	ПОТУЖНІСТЬ, Вт/м²
1	849.68	7,70

ШИНОПРОВІД ТА АКСЕСУАРИ

№	ПОЗНАЧЕННЯ	НАЙМЕНУВАННЯ	К-сть, шт.
1	1M	Шинопровід трифазний 1м (IP20 16A 400V)	11
2	2M	Шинопровід трифазний 2м (IP20 16A 400V)	4
3	3M	Шинопровід трифазний 3м (IP20 16A 400V)	6
4		Живлення	16
5		Заглушка для шинопроводу	16
6		З'єднувач лінійний шинопроводу	5
7		ЛІНІЙНА ФІКСУЮЧА ДЕТАЛЬ	5
7		Кронштейн підвісний (комплект для кріпл. шинопроводу для кріпл. обшивки, кабелю, дротів, обшив з кімнатою, світіль)	52
8		Трос, м	156

СПЕЦИФІКАЦІЯ МОНТАЖНИХ КОМПЛЕКТІВ ЛІНІЙНИХ СВІТИЛЬНИКІВ

№	НАЙМЕНУВАННЯ	К-сть, шт.
1	Монтажна арматура для кріплення підвісний світіль: фіксуючий для кріпл. шинопроводу для кріпл. обшив, кабелю, дротів, обшив з кімнатою, світіль	120
2	Трос, м	260

НАПРЯМ СВІТЛА ЛІНІЙНИХ СВІТИЛЬНИКІВ Z-ZA

ВВІД ЖИВЛЕННЯ ЛІНІЙНИХ СВІТИЛЬНИКІВ

9 НОМЕР МАГІСТРАЛІ

ВИСОТА МОНТАЖУ ШИНОПРОВОДУ 3 МЕТРИ ВІД РІВНЯ ПІДЛОГИ

ВИСОТА МОНТАЖУ ЛІНІЙНИХ СВІТИЛЬНИКІВ ТИПУ Z - ZA 2.8 МЕТРИ ВІД РІВНЯ ПІДЛОГИ

ВИСОТА МОНТАЖУ ЛІНІЙНИХ СВІТИЛЬНИКІВ ТИПУ X - XA 2.8 МЕТРИ ВІД РІВНЯ ПІДЛОГИ

ВИСОТА МОНТАЖУ ЛІНІЙНИХ СВІТИЛЬНИКІВ ТИПУ X - XA 3.1 МЕТРИ ВІД РІВНЯ ПІДЛОГИ

ВИСОТА МОНТАЖУ ЛІНІЙНИХ СВІТИЛЬНИКІВ ТИПУ I-IA 2.8 МЕТРИ ВІД РІВНЯ ПІДЛОГИ

Зм.	Кілк	N°докум.	Підп.	Дата	СО		
Розроб.					СУПЕРМАРКЕТ "АТБ" г. Черкассы, бул.Шевченка, 145	Стадія	Аркуш	Аркушів
Перев.								
Т.контр.								
Н.контр.					СХЕМА ОСВІТЛЕННЯ			
Затв.								